PLAN (y up = hydroponic wall, as printed top of ICES Fig 2)

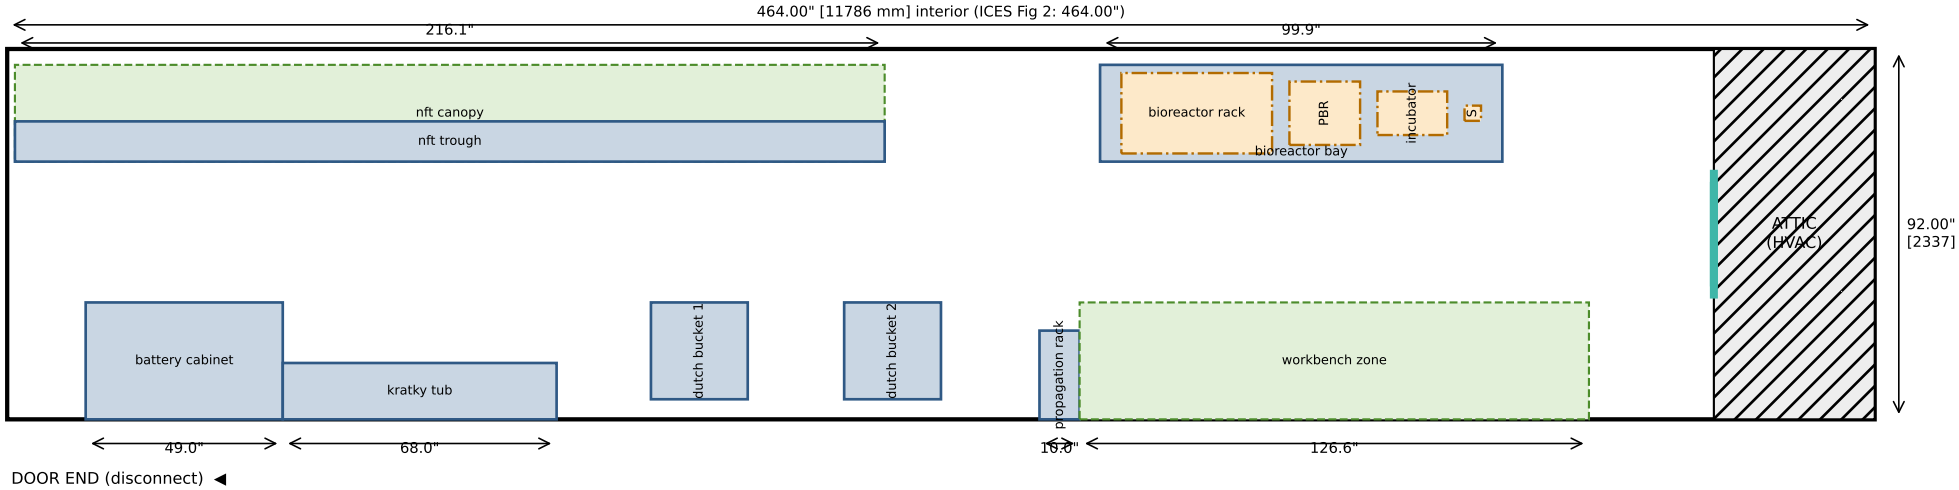

ELEVATION A — hydroponic / bioreactor-bay wall (door end left)

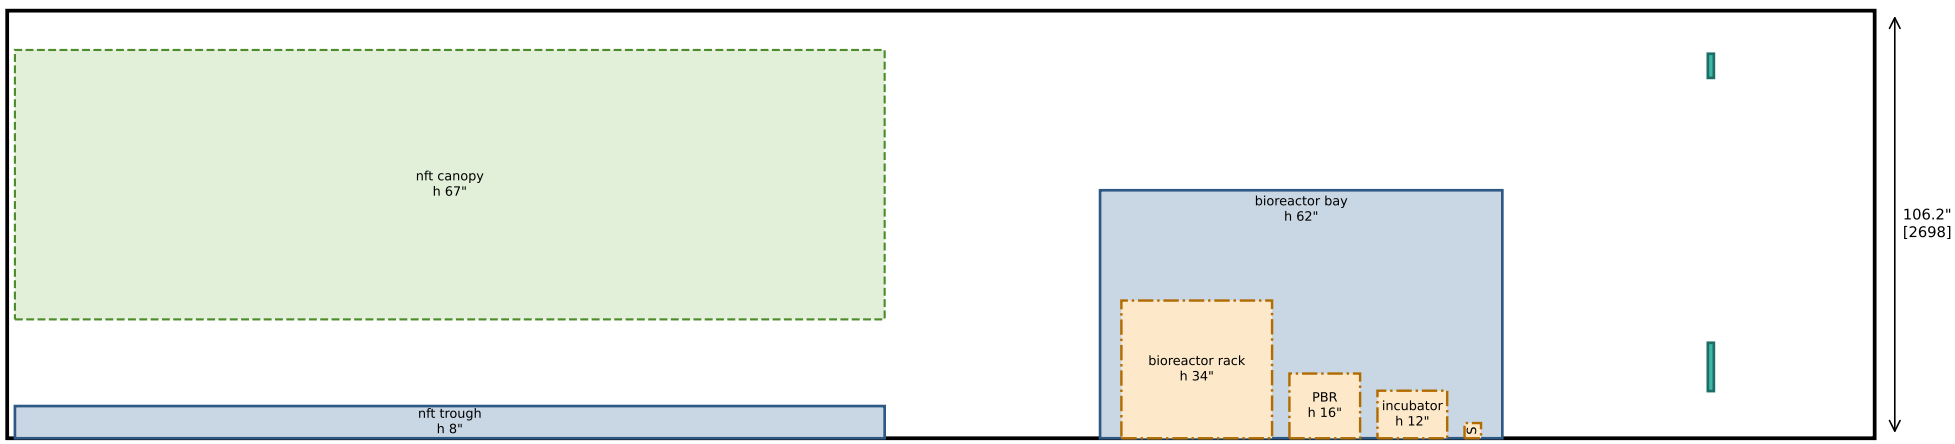
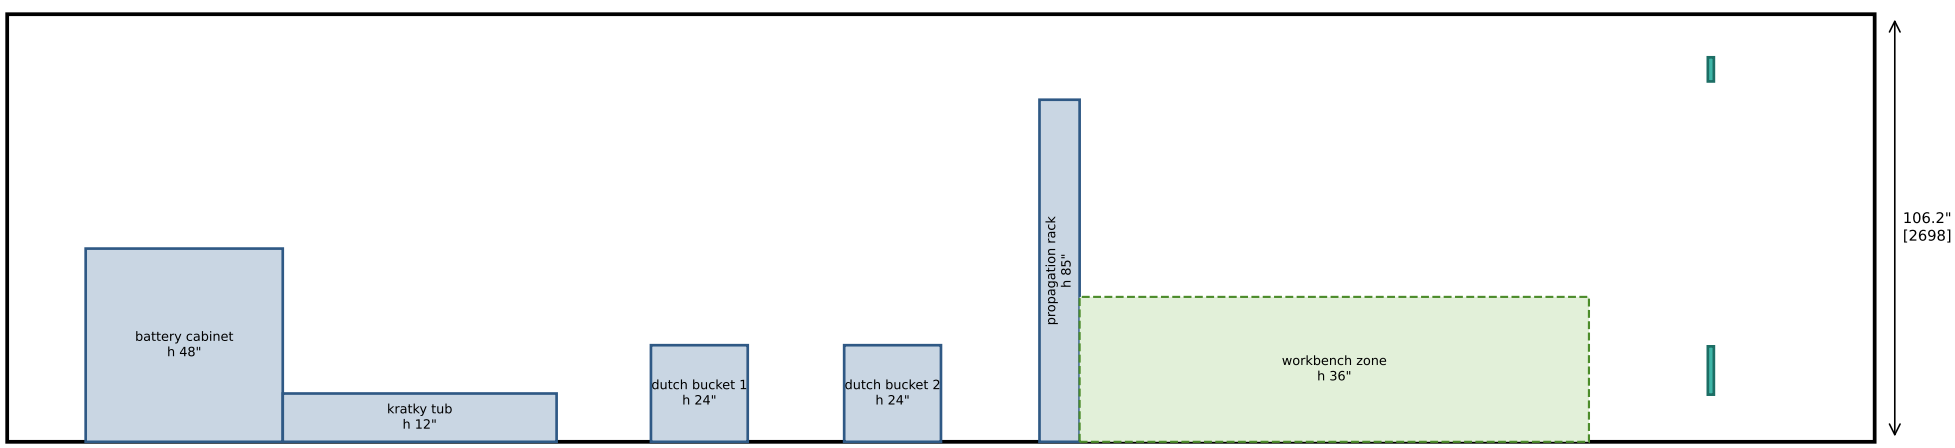
ELEVATION B — battery / work-space wall (door end left)